

EXAMEN FINAL : CURSO CONCRETO ARMADO - II

Apellidos y Nombres:..... Cod. Matricula:.....

Fecha: 04/08/2020 Firma:


1.- Dimensionar, Verificar, Diseñar y mostrar el detalle el armado final la zapata aislada que soportar una columna de sección rectangular de 0.30x0.50 m. (bxt), reforzada con 6Ø3/4” para las siguientes solicitaciones estructurales:

$P_{wd} = 62.50 \text{ Ton.}$ $M_{wd} = 1.125 \text{ Ton-m}$

$P_{wl} = 42.50 \text{ Ton.}$ $M_{wl} = 0.695 \text{ Ton-m.}$

El nivel de fundación está a 2.10 m. por debajo del N.P.T. , el suelo conforma tres estratos los pesos específicos son $\gamma_{s1}=1.45 \text{ ton/m}^3$, $\gamma_{s2}=1.55 \text{ ton/m}^3$, $\gamma_{s3}=1.85 \text{ ton/m}^3$, considere los pesos específicos en piso incluye acabados $\gamma_p=1.75 \text{ ton/m}^3$, peso del solado $\gamma_s=1.95 \text{ ton/m}^3$, sobrecarga de servicio S/C= 450 kg/m² , según estudio de mecánica de suelos la capacidad portante es de $\sigma_t=2.425 \text{ kg/cm}^2$, considerar para el diseño $f'_c=220 \text{ kg/cm}^2$ y $f'_y=3900 \text{ kg/cm}^2$.

Nota: Usar las Normas (E-060) del RNE.

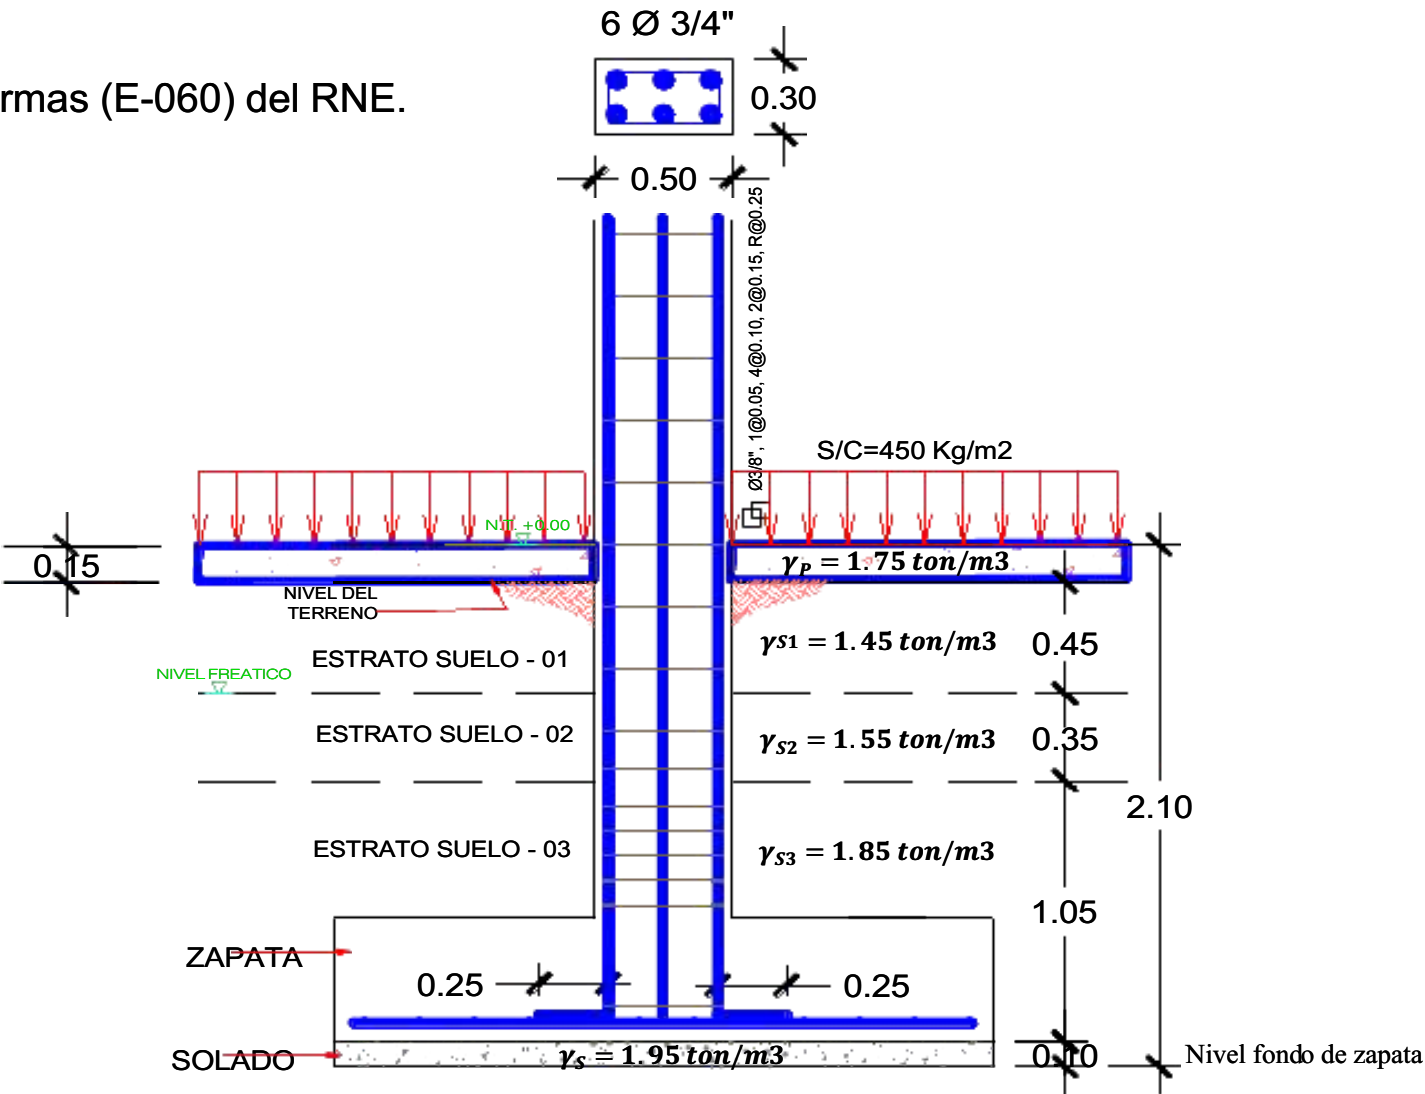

Hora de Inicio : 8 : 30
Hora de termino: 10: 30

Nota 02: Al término del examen reenviar la resolución del examen a la dirección de la delegada del curso aldy.coaquira@upeu.edu.pe